

PORTFOLIO

LUCAS POUPINOT





**POUPINOT
LUCAS**

**Paysagiste
Concepteur**

**+ 33 6 52 67 38 20
lucas.poupinot@gmail.com**


EXPÉRIENCES

- Été 2025**
CDD à Cour Saint Saut (59)
Barman et participation à la gestion d'un lieu culturel transitoire
- 2024**
CDD ouvrier horticole - Pépinière de Gruson (59)
Lien entre production, entretien et intégration dans le projet
Connaissances essences et techniques de cultures
- Été 2023**
Mission Eau et Environnement au département du Nord -
Stage maîtrise d'ouvrage
Rédaction d'un dossier de synthèse règlementaire et prescriptif
- Été 2022**
Agence Empreinte (59) - Stage maîtrise d'oeuvre
Coupes de projet d'espaces publics NPNRU
Plans topographiques Autocad projet Grand Euralille
Familiarisation avec le déroulement d'un projet d'espace public
- Été 2021**
Agence SLAP Paysage (59) - Stage maîtrise d'oeuvre
Illustration et rédaction de dossiers circuit cyclable MEL
- Été 2020**
Ouvrier agricole maraichage biologique - Jardins de l'Osme (16)
Ouvrier - Jardin des Plantes de Lille (59)
- Été 2019**
Serveur en restauration - La Bottega (59)

LOGICIELS

Indesign
Photoshop
Illustrator
Qgis
Autocad
Sketchup

LOISIRS

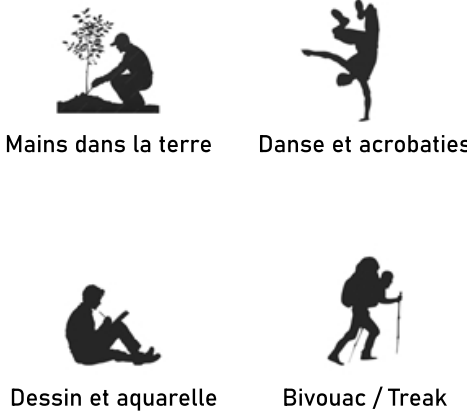

Mains dans la terre
Danse et acrobaties
Dessin et aquarelle
Bivouac / Treak

4 PROJETS DE PAYSAGE

PRODUCTIONS ANNEXES

NUANCE D'ENROBÉ

Recoloniser des sols imperméables à moindre coût



Atelier morphologie végétal
encadré par François-Xavier Mousquet et Dominique Henry

L'attendu de l'atelier était de concevoir une stratégie végétale, c'était l'occasion pour moi de travailler sur un sujet qui me passionne : la désimperméabilisation.


Au sein d'un espace public majoritairement bétonné et dénué de fonction, nous avons imaginé en binôme un jardin expérimental explorant différentes manière de déstructurer le sol pour favoriser le développement d'une végétation dans le temps.

Différents outils de mise en œuvre et techniques de plantation ont été mobilisés. L'objectif était de mettre en place un processus évolutif, économe en ressources, permettant de laisser ou de réemployer sur place les débris.


Il s'agissait également de créer des microclimats pour diversifier les conditions écologiques du site, en jouant sur l'exposition, la micro-topographie et l'inertie thermique des matériaux, afin d'accueillir une diversité floristique plus large et durable dans les années à venir.

La palette végétale privilégie des essences présentes sur le site, des espèces pionnières adaptées aux milieux pauvres et des plantes typiques de milieux caillouteux, dont les systèmes racinaires contribuent au décompactage du sol, tout en veillant à une cohérence de textures et de teintes.




Les tracés de cet espace public ont été conçus pour pouvoir s'étendre à l'emplacement des barres d'immeubles adjacentes vouées à la démolition, permettant de réutiliser les gravats in situ, directement dans le jardin ou comme matériau pour le mobilier urbain.

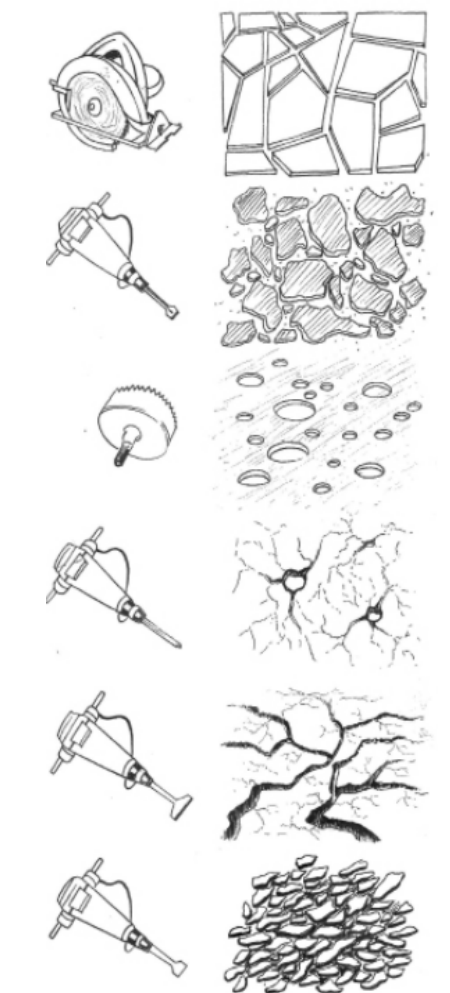

DÉCOUPER
CONCASSER
PERFORER
FISSURER

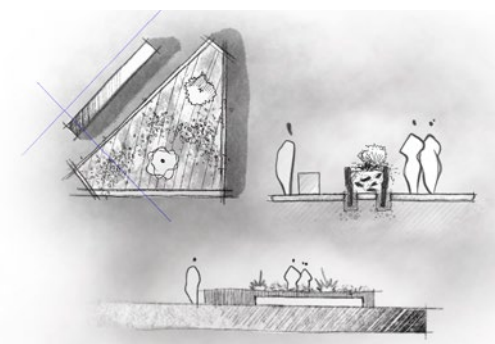

Mobilier réutilisant les matériaux du chantier

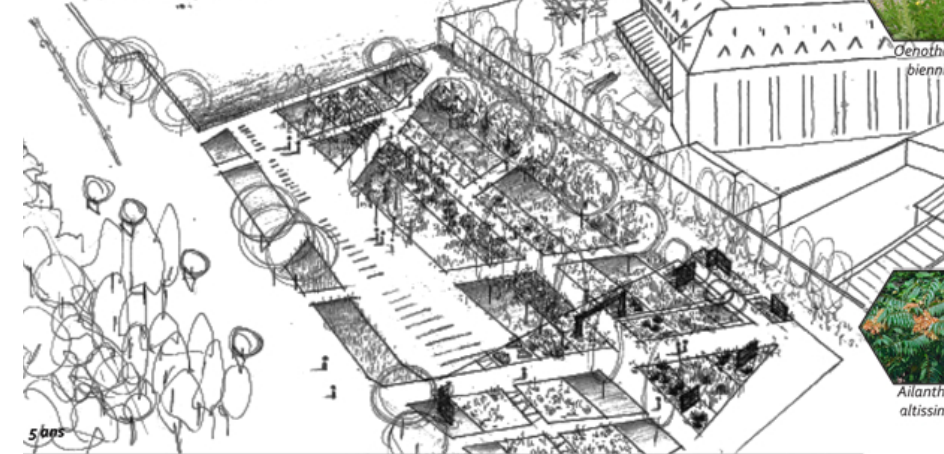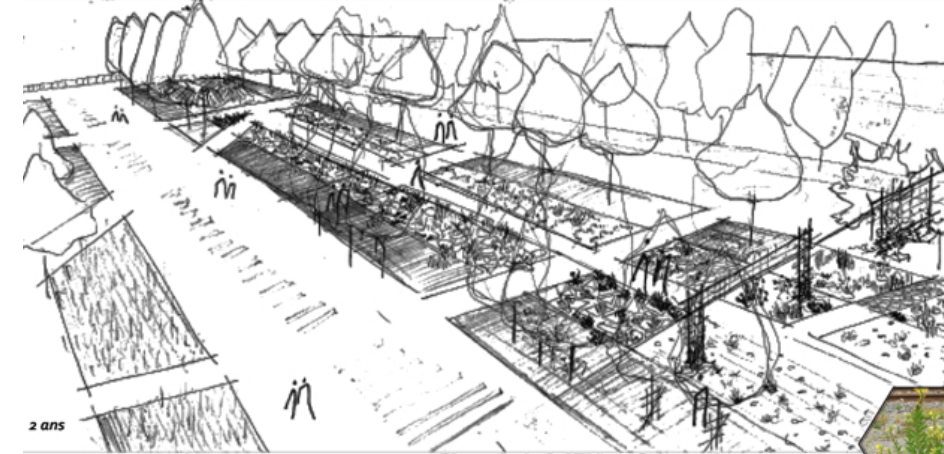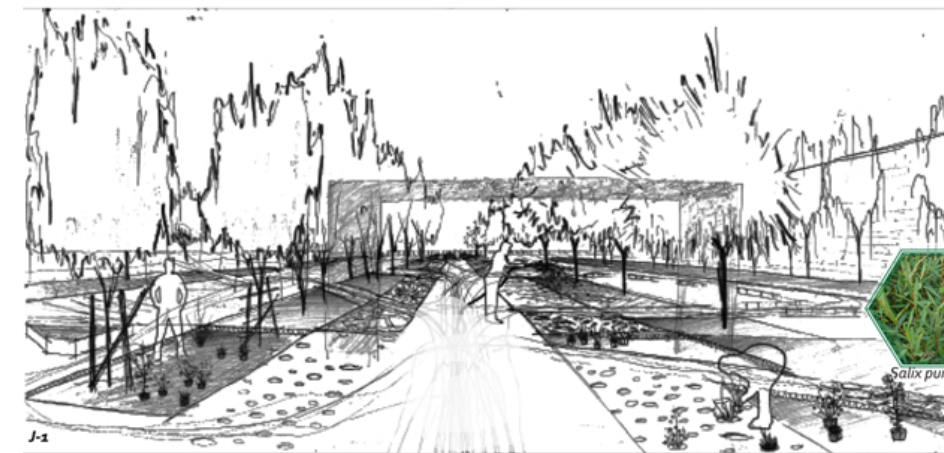


HYDROSEEDER
SEMIS
BOUTURE
POQUETS



LE CHAMP DES POSSIBLES

Imaginer une résilience urbaine

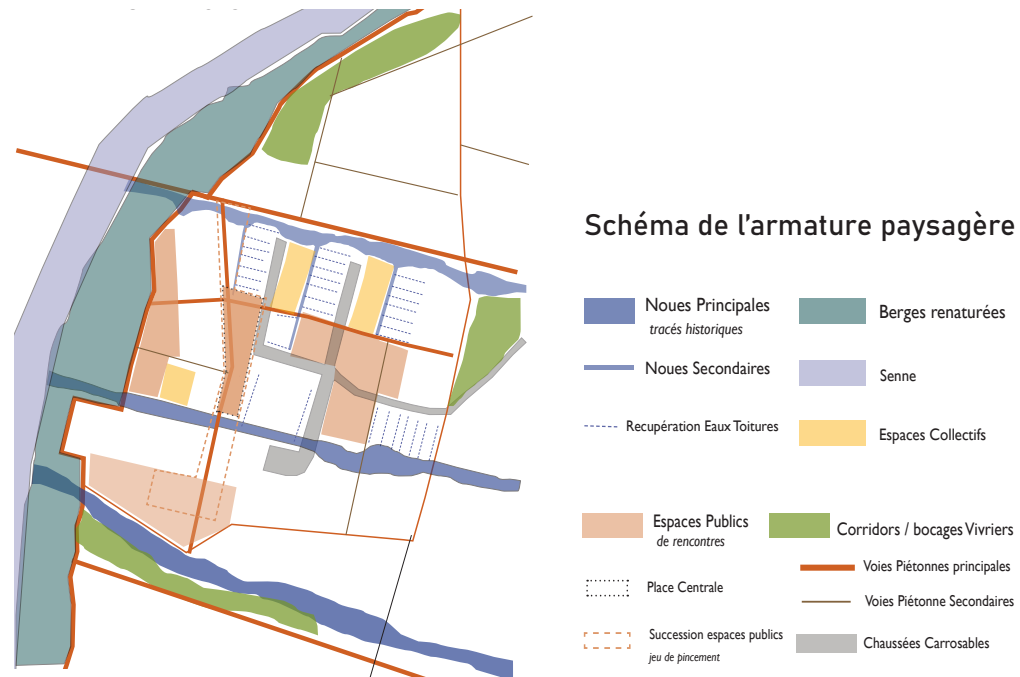


Atelier ville productive
encadré par Aurélien Zoia et Antoine Béal

Sur une vaste friche industrielle belge, l'ambition dépassait le projet alliant l'architecte et le paysagiste pour **proposer un modèle socio-économique répondant aux enjeux systémiques contemporains.**

La place de l'**activité nourricière** et la **gestion de l'eau** deviennent **structurantes**. Des noues servent par exemple de seuil entre logements et espaces cultivés et guident les déplacements jusqu'aux berges en reprenant les tracés historiques des voies ferrées.

Que ce soit dans les modes de productions (forêt-jardin, maraîchage...), de construction, de dépollution, de déplacements ou de développement urbain ; ce travail m'a permis de tester des **stratégies durables et adaptables** à diverses échelles et contextes.

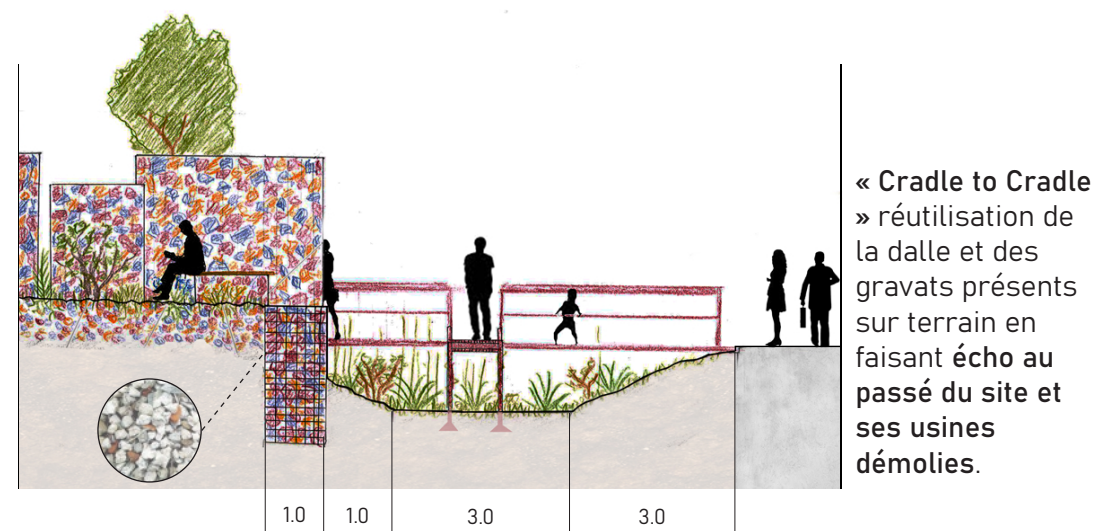

Maquette en binôme 1 / 500e



Maquette en groupe 1 / 1000e

Éclairage architectural- Coupe 1 / 200e façade du silôt

Jouer avec les ombres des végétaux, réglette LED intégrée à jardinière




Plan masse lumière 1 / 500e

'Ramener' graphiquement le rural dans l'urbain et vice versa



DE LA CULTURE DU GREEN À LA CULTURE D'UN SOL COMMUN


Habiter autrement les paysages golfixques

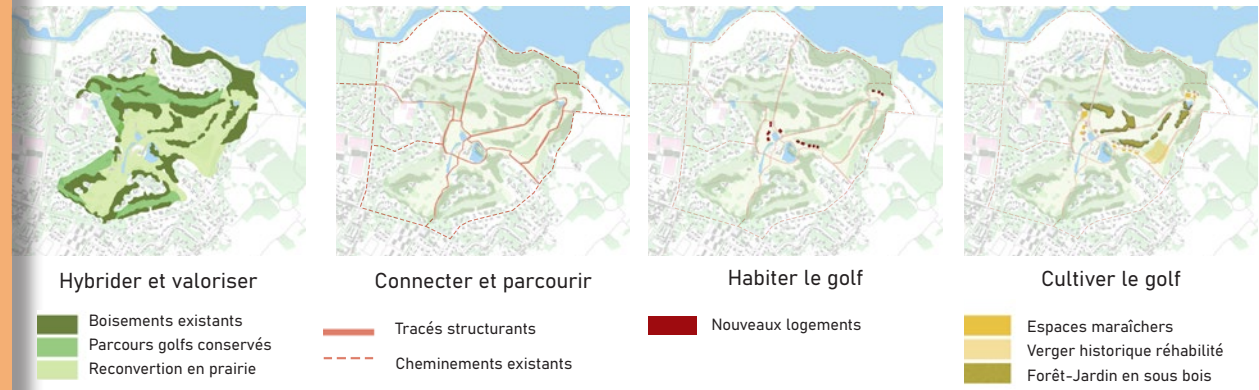

Atelier lotissement autrement encadré par Sabrina Hiridjee et Claire Laubie

Ce projet imagine la transformation partielle d'un golf sans contact avec les **'grands paysages'** environnants (lac, champs). Le parti pris vise à **rendre accessible à tous un lieu remarquable** et questionner le devenir de ce type d'espaces face aux enjeux de demain.

Trois **'micro-hameaux'** où **architecture et paysage se répondent**, sont implantés en lien avec les boisements centenaires et plans d'eau existants en **préservant l'étendue et les qualités du site**. Le projet favorise la **mixité sociale** et **l'attachement** des habitants à leur milieu de vie, notamment par une offre de **74 logements diversifiés**, des espaces de cultures et de circulation partagés, tout en visant une **renaturation des milieux anthropisés**.

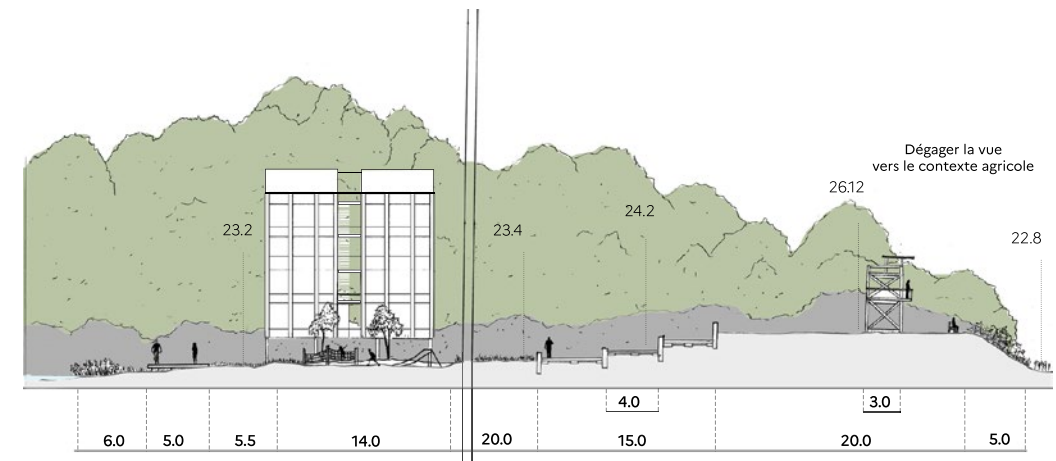

Faire écho aux troncs par la structure bâti qui cadre des vues, limite l'emprise au sol et évoque l'idée de grimper aux arbres



Réutiliser les bunkers de sables, composer avec l'identité du site




Maquette de travail 1 / 100e

UNE INTERFACE ENTRE QUARTIERS ET MÉMOIRE MINIÈRE

Faire émerger une nouvelle centralité à partir du patrimoine


1 - SERVICES ÉCOSYSTÉMIQUES

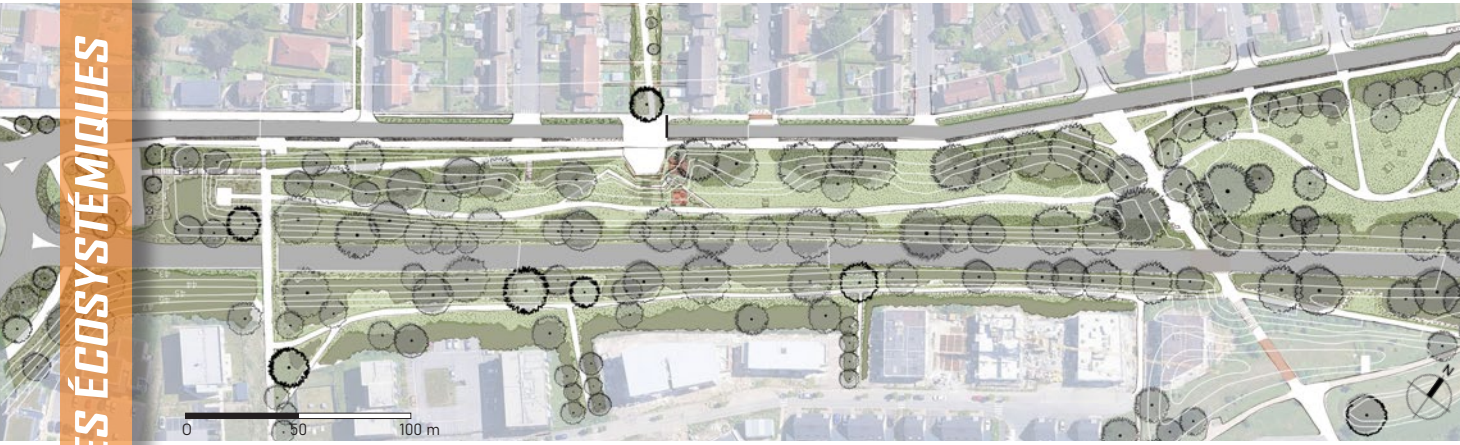

Atelier services écosystémiques encadré par Yves Hubert

Au cours de cet atelier, nous avons créer un jeu de cartes pour saisir les enjeux d'une commune du bassin minier à travers la parole habitante.

Le projet d'un parc fédérateur entre les quartiers s'appuie sur des talus hérités de l'ère minière et met en lumière différents éléments patrimoniaux tout en transformant la fracture routière en une continuité paysagère. Pensé pour les usages quotidiens, le parc se prolonge dans les rues et s'articule avec les espaces publics. La véloroute existante, dont le tracé est confortée, devient le fil narratif de l'histoire du territoire.

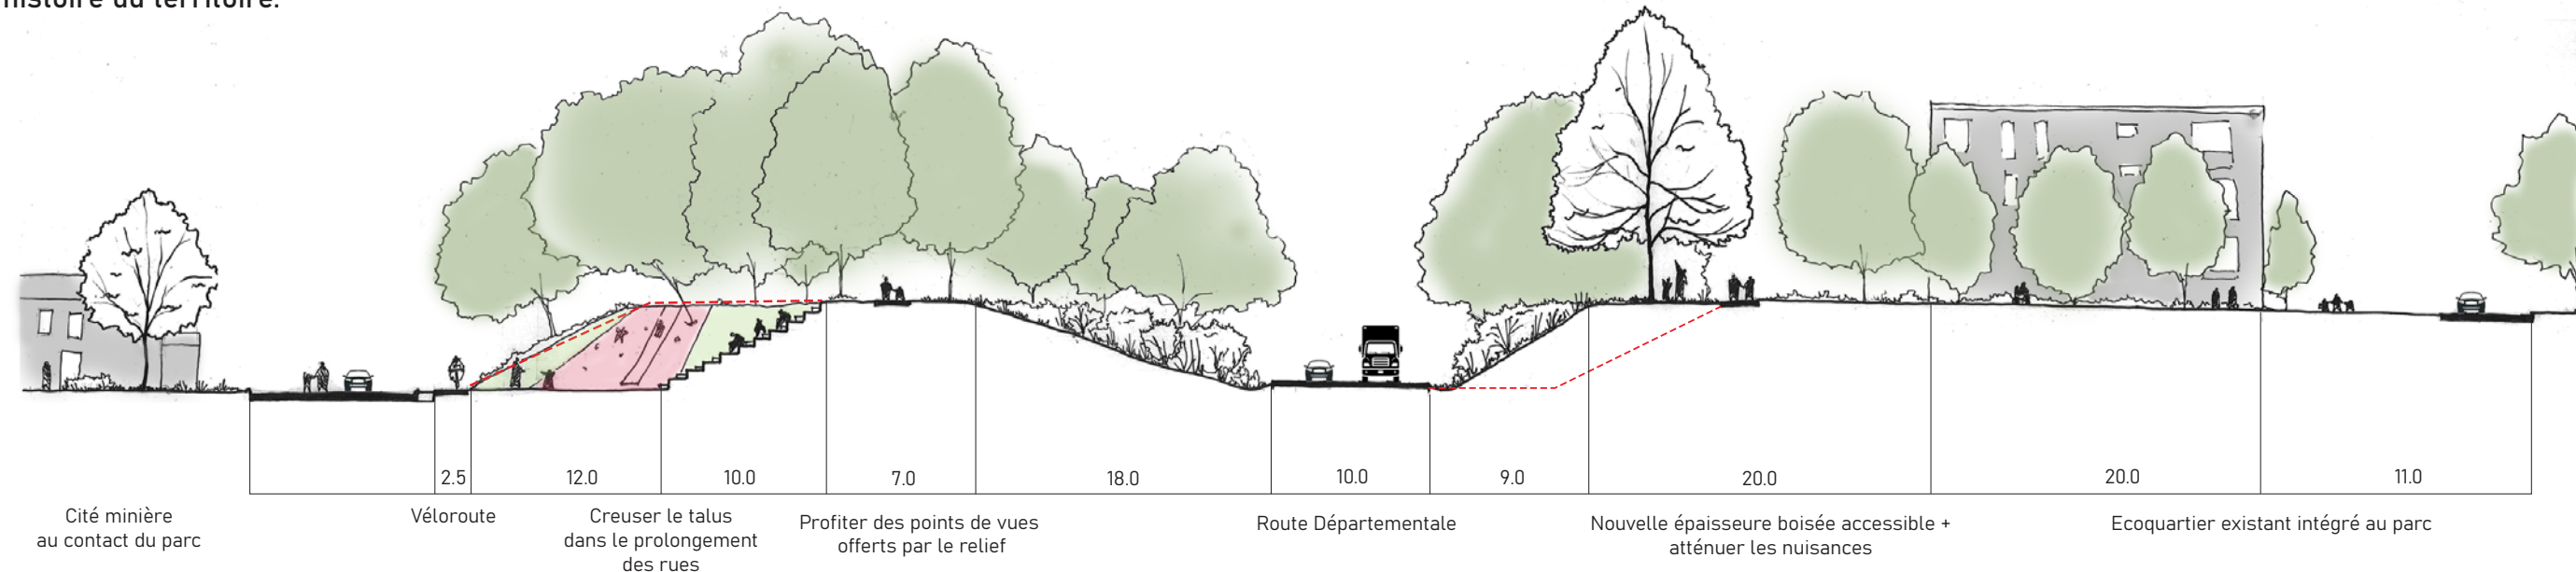


PRODUCTIONS


ANNEXES

Travaux réalisés en agences sur Autocad

Documents de projet de renouvellement urbain à Lille

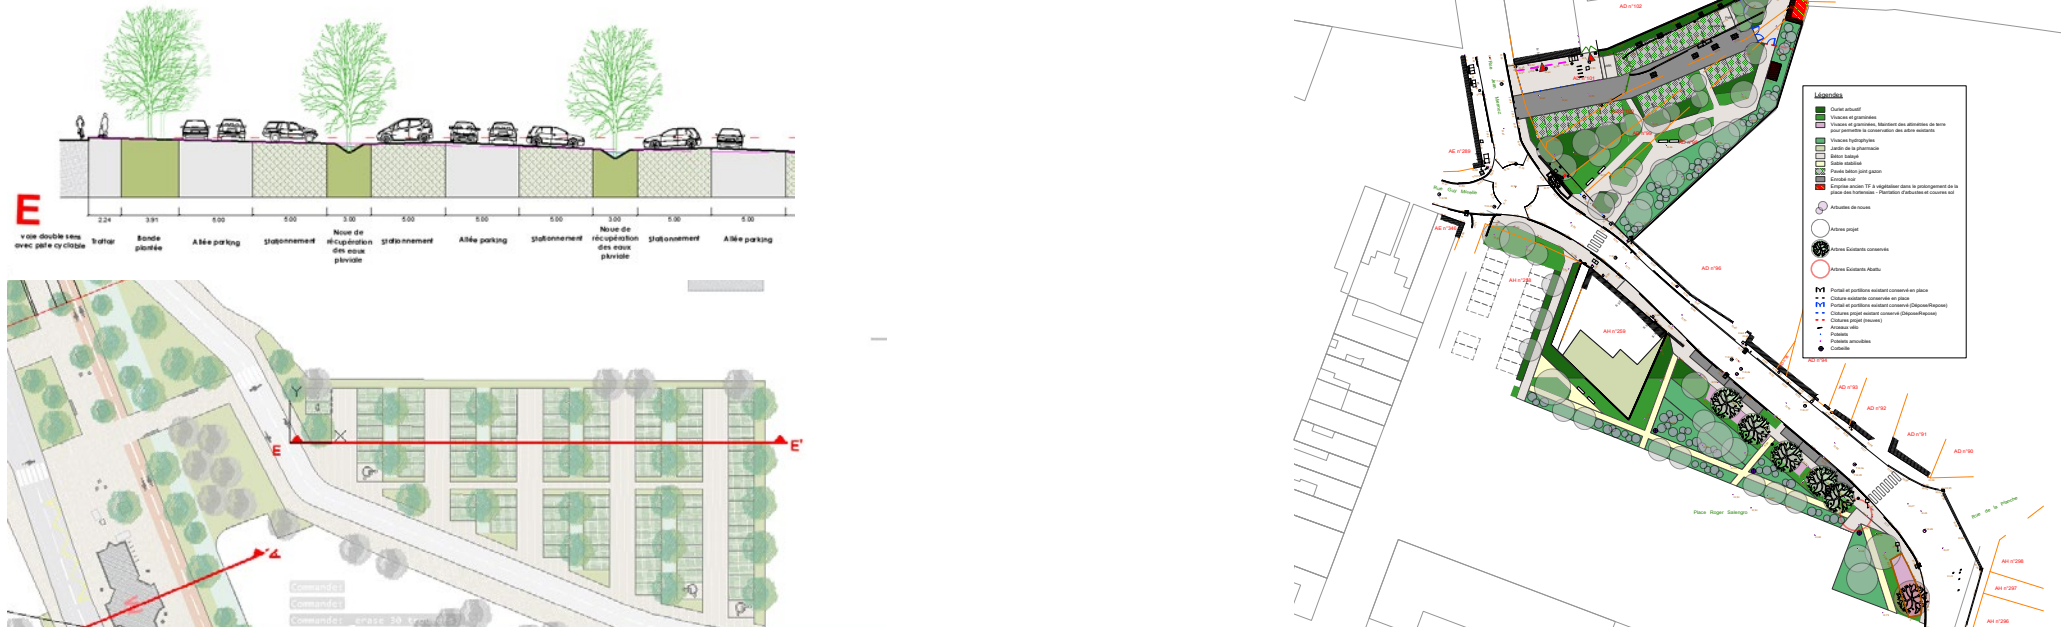

Plans topographiques pour découpe laser - Projet Grand Euralille

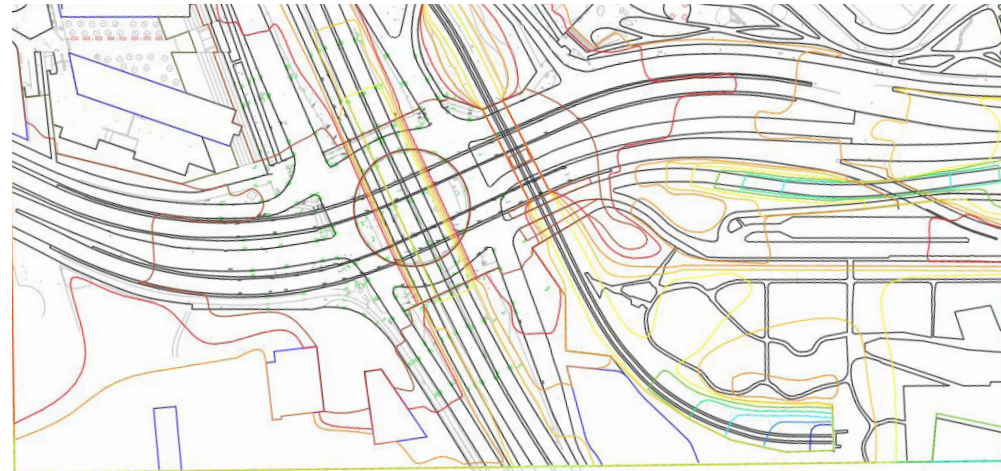


Mémoire mention recherche sur l'analyse des usages à travers la perception des seuils - Réserve Naturelle Régionale du Héron



Dessins d'ambiances réalisés en Haut de France



Échappée paisible vers les joyaux du bocage

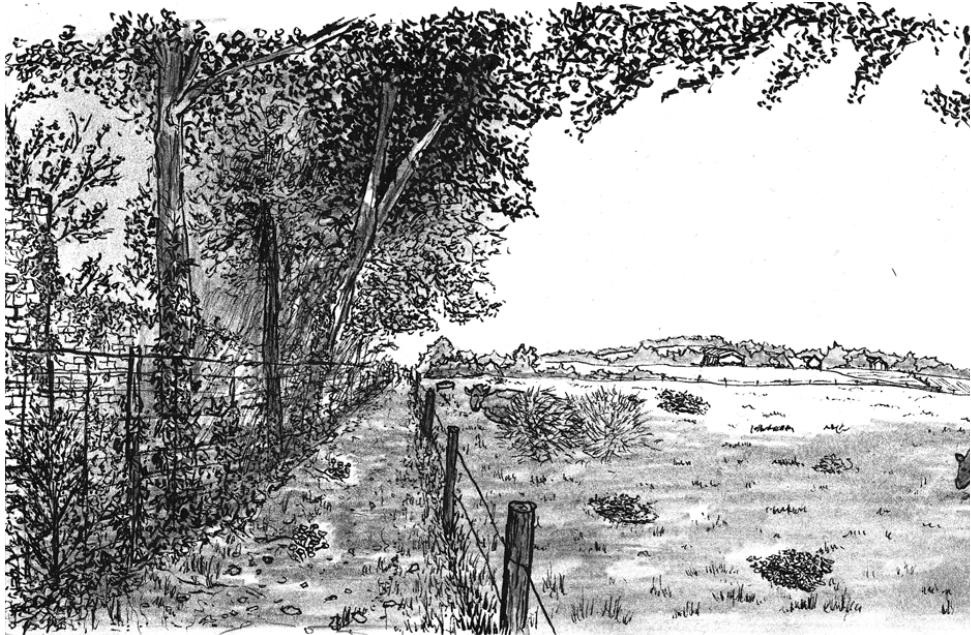

Épouser la lisière, embrasser l'horizon



Attiser la curiosité à travers champs





Déambuler au gré des ombres





Série d'aquarelles réalisée pour
une commune du Bassin Minier
Méricourt (62)

Coupes perspectives projectuelles

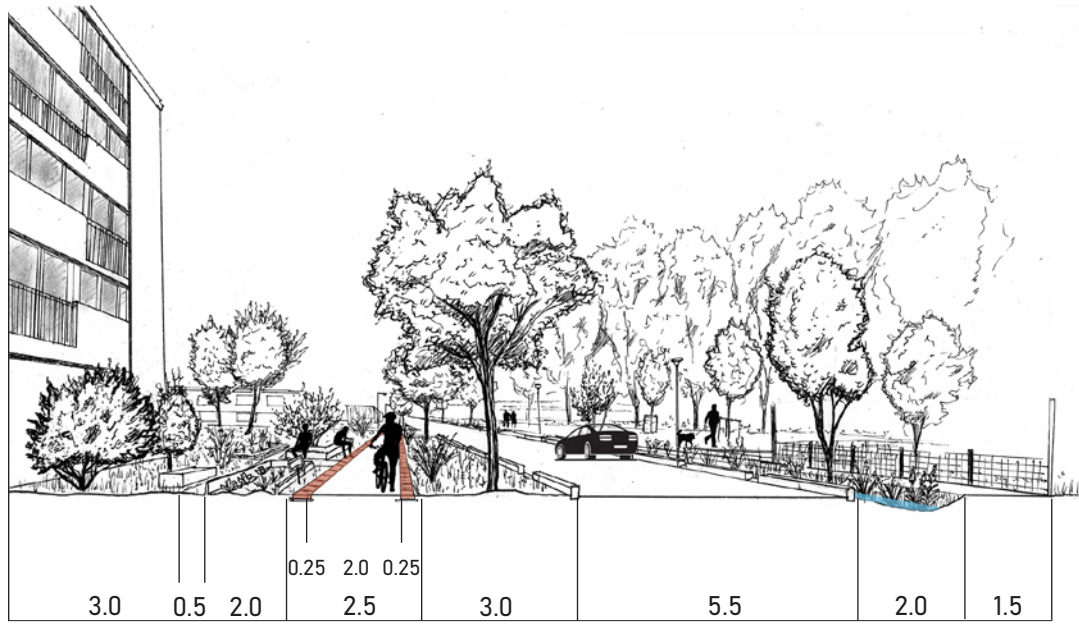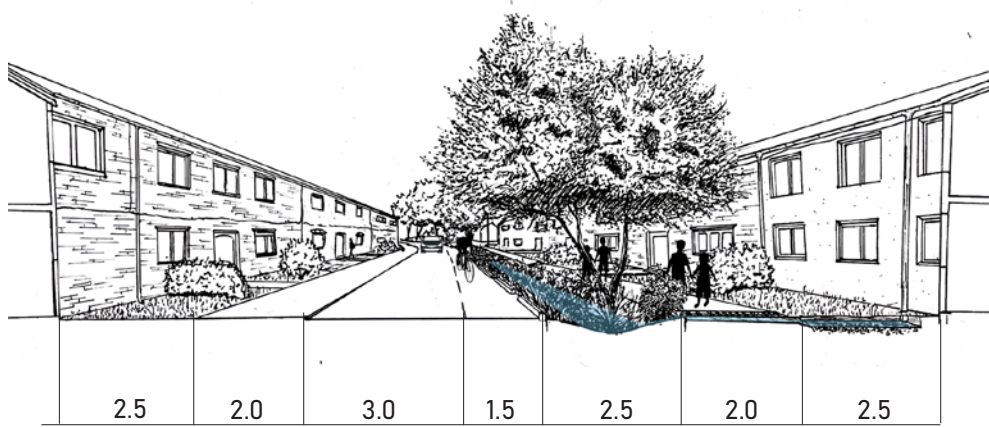

Analyse spatiale plan-coupe
gestion des eaux et des seuils espaces publics-privés

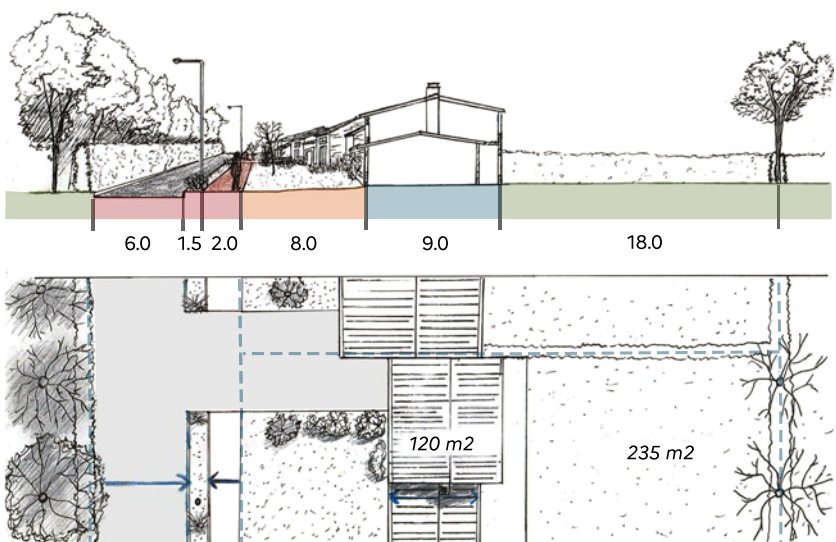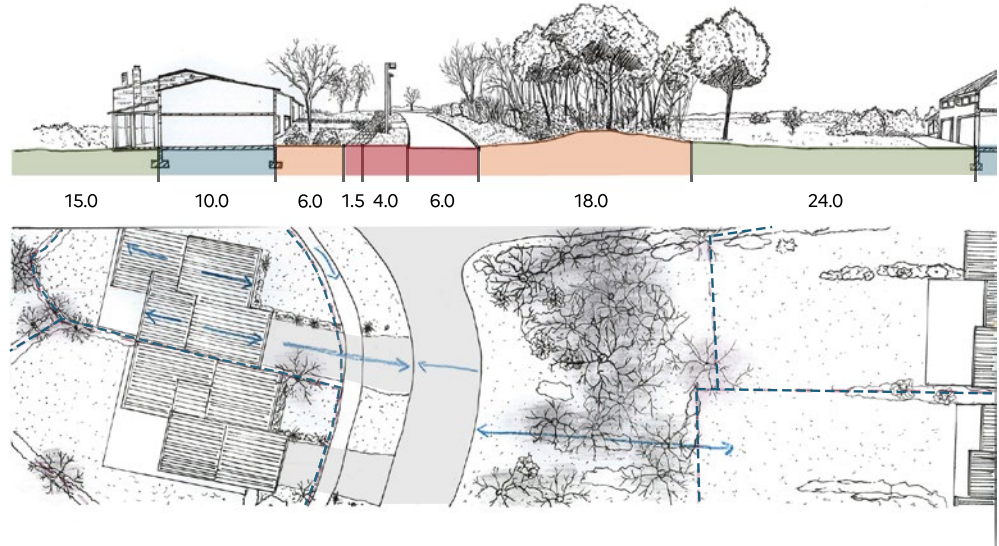

Les fonctions de la haie

Le bocage, composante polyvalente du paysage agricole,
garante de sa qualité et de son maintien



Intérêts paysagers

- structure et délimite les espaces
- cadre et met en scène des vues,
- rythme les étendues agricoles et brise leur monotonie (contraste, jeu ouvert-couvert, lumière-ombre),
- crée des ambiances, des lieux
- intègre voir sublime l'architecture



Intérêts lié aux usages quotidiens

- repère visuelle, signale et guide les trajets
- anime et conforte les parcours
- protège du vent, offre de l'ombre et des îlots de fraîcheur




Intérêts écologiques

Les haies offrent habitats et ressources alimentaires à de nombreuses espèces animales, incluant insectes, oiseaux et mammifères. Elles constituent des corridors écologiques essentiels à la biodiversité, et, par extension, au bien-être des humains.



Intérêts agricoles



- protège les cultures du vent
- limite l'évapotranspiration et les besoins en eau
- abrite des auxiliaires de cultures, diminution des ravageurs et maladies par régulation naturelle
- amélioration des sols, stimule l'activité biologique par apports de matière organique
- production de ressources complémentaires (bois de chauffage, de construction, paillage...)
- favorise la pollinisation

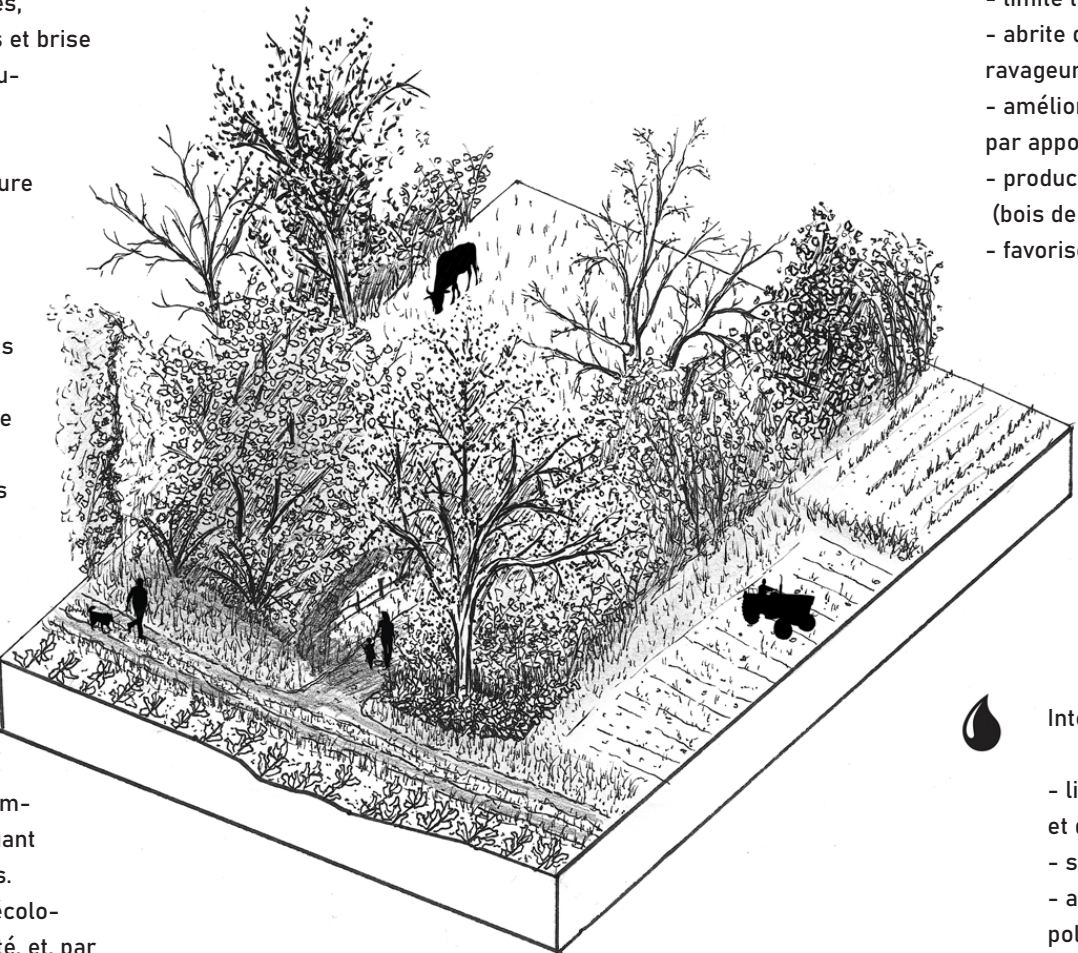

Intérêts hydrauliques

- limite les risques : d'érosion, de coulée de boue et d'inondation lié au ruissellement,
- stocke l'eau proche des cultures,
- améliore la qualité de l'eau (filtre sédiment et polluants),
- favorise le rechargement des nappes par infiltration

Carnet de voyage dans les Pyrénées au feutre noir et à l'aquarelle

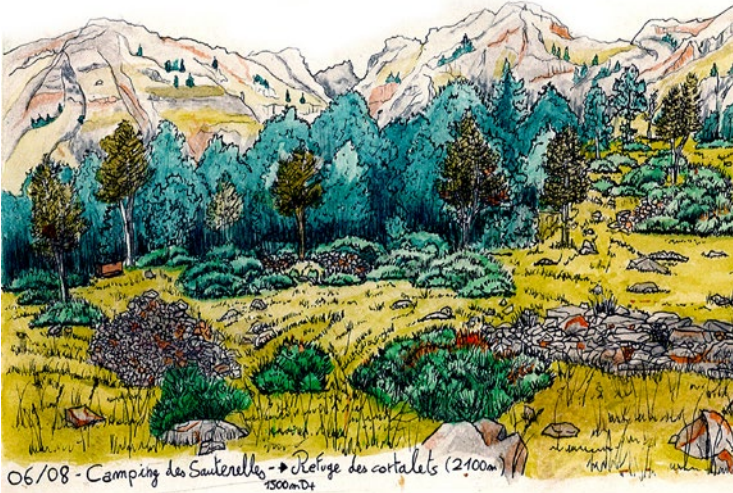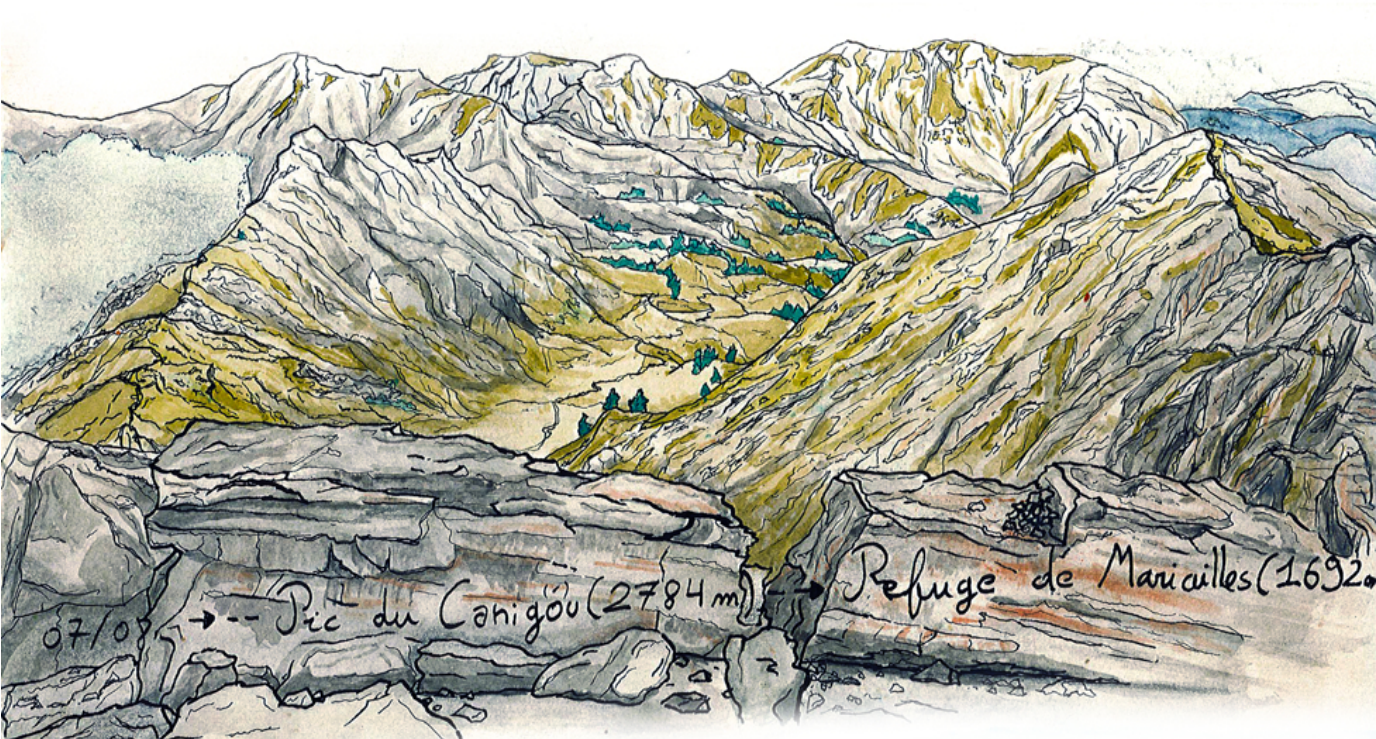

Coupe au feutre noir réalisée durant l'atelier « Morphologie végétale »

